SUP. APROX. SEGUN PLANO TOPOGRAFÍA 5.153 M^2

TOTAL ÁREA
SUP. 5.125 M^2
S/LOTEO LOTE 30-1

CUADRO DE ZONAS, DENSIDAD Y COBERTURA (Manual §3.3.5 - §3.3.6)

ZONA	TIPOLOGÍA	SUP. PLANT. m²	N° SP.	ÁRB.	ARB.	HERB.	CUBR.	TOTAL	PL/m²	COB. INICIAL	COB. DESARR.	ESP. ABIERTO
B-2	● Bandejón Acceso/salida	861.8	8	0	327	60	159	546	0.63	4 %	62 %	38 %
B-1	● Bandejón Acceso/salida	142.2	5	0	40	25	59	124	0.87	6 %	44 %	56 %
B-3	● Bandejón Acceso/salida	407.1	6	0	205	12	66	283	0.70	5 %	56 %	44 %
B-4	● Bandejón Acceso/salida	16.8	2	0	14	19	0	33	1.96	13 %	28 %	72 %
I-1	● Islas	284.7	8	5	85	46	84	220	0.77	6 %	49 %	51 %
I-2	● Islas	61.2	5	1	17	8	23	49	0.80	6 %	40 %	60 %
I-3	● Islas	20.8	4	1	3	7	16	27	1.30	10 %	55 %	45 %
I-4	● Islas	161.0	7	2	29	32	61	124	0.77	6 %	44 %	56 %
T-1	● Tienda Y Terraza	38.3	5	2	13	17	13	45	1.17	9 %	57 %	43 %
T-2	● Tienda Y Terraza	16.8	3	0	0	18	9	27	1.61	11 %	21 %	79 %
T-3	● Tienda Y Terraza	18.5	4	1	7	4	0	12	0.65	6 %	69 %	31 %
T-4	● Tienda Y Terraza	5.3	2	1	0	5	0	6	1.14	14 %	98 %	2 %
T-5	● Tienda Y Terraza	6.3	3	1	1	0	5	7	1.12	11 %	71 %	29 %
T-6	● Tienda Y Terraza	2.7	1	0	0	0	5	5	1.88	13 %	50 %	50 %
T-7	● Tienda Y Terraza	8.0	2	0	0	14	0	14	1.74	12 %	16 %	84 %
P-1	● Bordes Perimetrales	79.6	5	9	18	16	41	84	1.05	11 %	84 %	16 %
P-2	● Bordes Perimetrales	115.8	6	6	28	21	85	140	1.21	10 %	74 %	26 %
TOTAL	**Jardín sustentable**	**2247.0**	**23**	**29**	**787**	**304**	**626**	**1746**	**0.78**	**6 %**	**57 %**	**43 %**

Superficie plantable = superficie de jardín descontando infraestructura existente (losa de estanques, cargadores EV, caseta Lavamax, luminarias, letreros). Cobertura desarrollada = proyección de copas adultas (año 4-5) sobre la superficie plantable; meta del Manual ~60 % (hasta 80 %). Densidades por estrato según §3.3.5: árboles 1 por copa, arbustos 0,5-1 pl/m², herbáceas 1-2 pl/m², cubresuelos 3 pl/m².

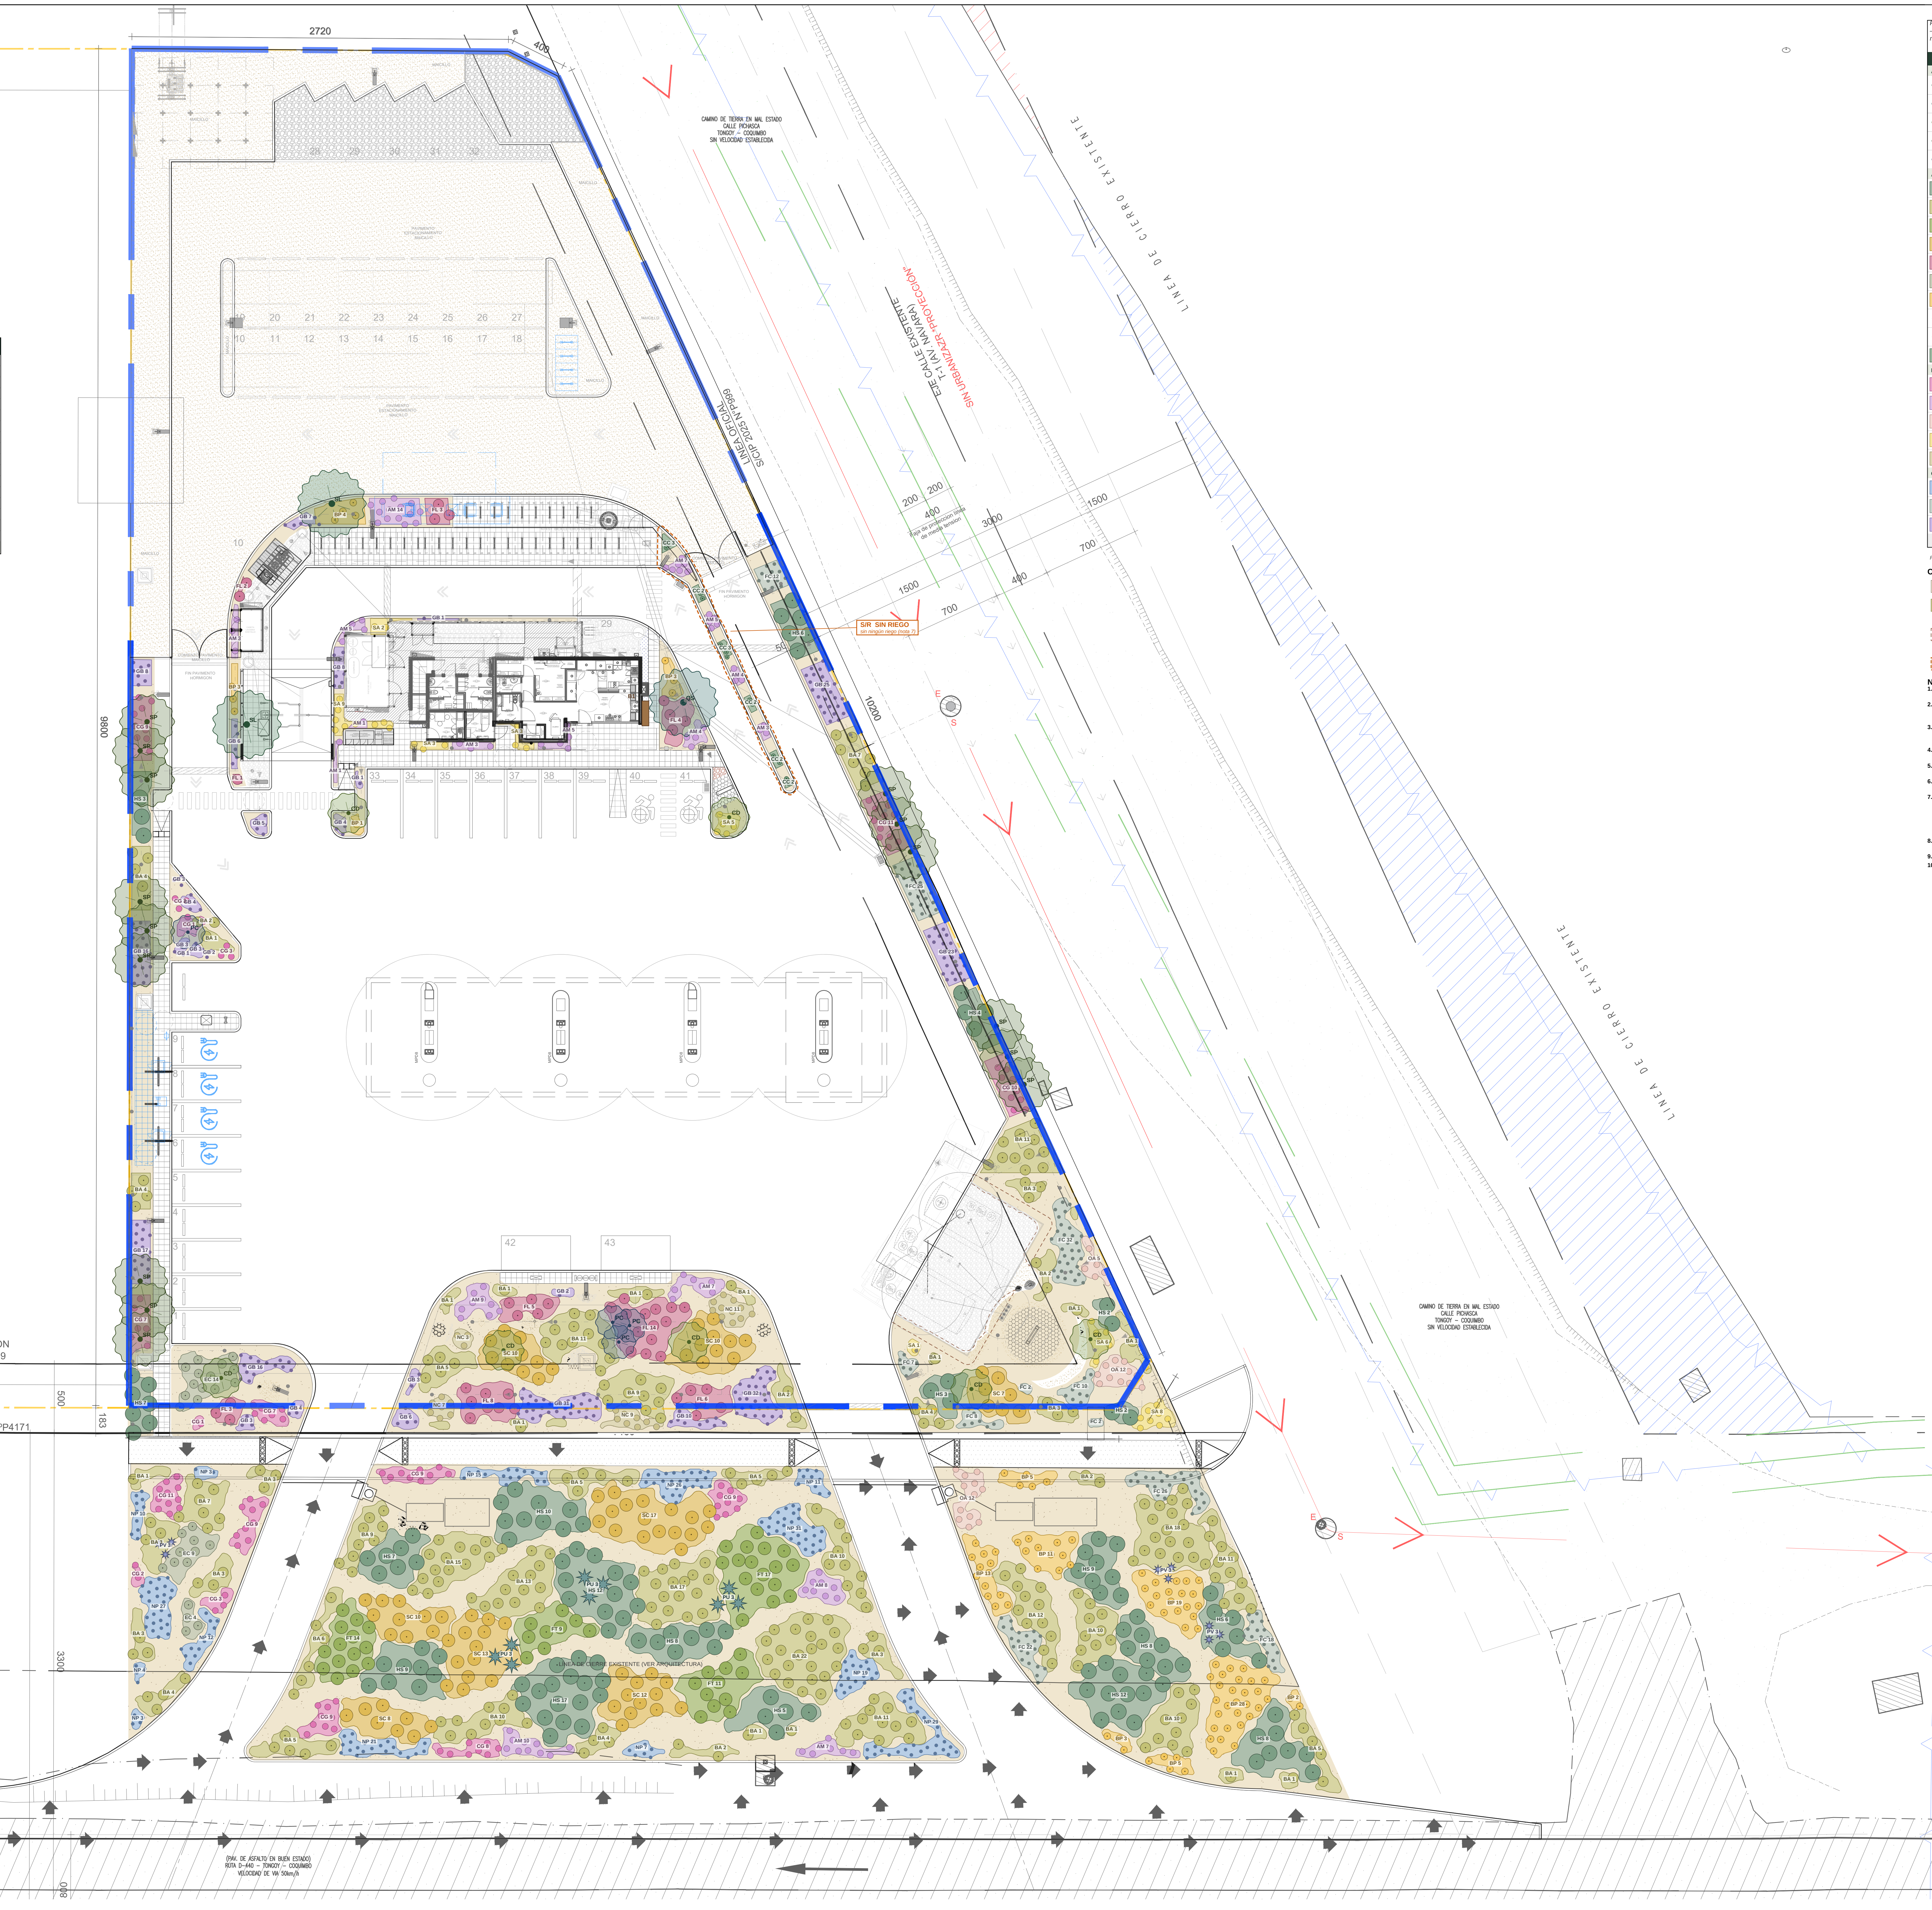

SIMBOLOGÍA PAISAJISMO

Paisajismo Ecosistémico COPEC. Ecosistema de referencia (Luebert & Pliscoff 2017, SIMBIO): Formación Matorral desértico — piso "Matorral desértico mediterráneo costero de Oxalis gigantea y Heliotropium stenophyllum" + pisos aledaños de la misma formación.

	CÓD.	ESPECIE (nombre científico / común)	ALT x DIÁM	FLORACIÓN	R.H.	CANT.
ÁRBOL (ESTRATO SUPERIOR)						
✳	SL	*Schinus latifolius* Molle · endémica	5.0x5.0	Primavera *crema*	B-M	**2**
✳	QS	*Quillaja saponaria* Quillay · endémica	6.0x5.0	Primavera-verano *blanca*	B-M	**1**
✳	CD	*Cordia decandra* Carbonillo · endémica	3.5x3.0	Primavera *blanca*	BAJA	**7**
✳	SP	*Schinus polygamus* Huingán · nativa	3.5x4.0	Primavera *crema*	BAJA	**15**
✳	PC	*Porlieria chilensis* Guayacán · endémica	3.0x2.5	Invierno-primavera *azul violeta*	BAJA	**4**
ARBUSTO / SUCULENTA (ESTRATO INTERMEDIO)						
■	HS	*Heliotropium stenophyllum* Palo negro · endémica	1.5x1.8	Fines invierno-verano *blanca aromática*	BAJA	**138**
■	BA	*Bahia ambrosioides* Chamiza · endémica	0.8x1.2	Primavera-verano *amarilla*	BAJA	**309**
■	FT	*Flourensia thurifera* Maravilla del campo · endémica	1.6x1.5	Fines invierno-primavera *amarilla*	BAJA	**51**
■	SC	*Senna cumingii var. coquimbensis* Quebracho del norte · endémica	1.5x1.5	Primavera-otoño *amarillo oro*	BAJA	**87**
■	FL	*Fuchsia lycioides* Palo de yegua · endémica	2.0x1.2	Invierno *rosada*	B-M	**46**
■	EC	*Encelia canescens* Coronilla del fraile · nativa	0.9x1.0	Primavera-otoño *amarilla*	BAJA	**27**
■	BP	*Balbisia peduncularis* Amancay / Copa de oro · nativa	0.8x0.8	Primavera *amarilla*	BAJA	**97**
✶	PV	*Puya venusta* Chagual chico · endémica	0.7x0.8	Primavera *azul violácea*	BAJA	**9**
✶	PU	*Puya chilensis* Chagual · endémica	1.5x1.5	Primavera *amarillo verdosa*	BAJA	**9**
■	CC	*Copiapoa coquimbana* Copiapoa de Coquimbo · endémica	0.3x0.5	Primavera-verano *amarilla*	MUY BAJA	**14**
HERBÁCEA / GEÓFITA / GRAMÍNEA (ESTRATO INFERIOR)						
▨	CG	*Cistanthe grandiflora* Pata de guanaco · endémica	0.3x0.5	Primavera-verano *magenta*	BAJA	**112**
▨	AM	*Alstroemeria magnifica* Lirio del campo · endémica	0.6x0.4	Primavera *rosa lila*	BAJA	**96**
▨	OA	*Oenothera acaulis* Don Diego de la noche · nativa	0.1x0.5	Primavera-verano *blanca a rosada*	BAJA	**29**
▨	SA	*Sisyrinchium arenarium* Ñuño · nativa	0.4x0.3	Primavera *amarilla*	BAJA	**37**
▨	NC	*Nassella chilensis* Coirón / flechilla · nativa	0.6x0.5	Primavera *panoja plateada*	BAJA	**30**
CUBRESUELO (ESTRATO INFERIOR)						
▦	NP	*Nolana paradoxa* Suspiro de mar · nativa	0.2x0.7	Primavera-verano *azul*	BAJA	**218**
▦	FC	*Frankenia chilensis* Hierba del salitre · nativa	0.3x0.6	Verano *blanco rosada*	BAJA	**164**
▦	GB	*Glandularia berteroi* Verbena chilena · endémica	0.1x0.6	Primavera-otoño *lila*	BAJA	**244**
		TOTAL PLANTAS (23 especies nativas, 0 exóticas)				**1746**

R.H.: requerimiento hídrico.

COBERTURAS Y ELEMENTOS

▨	Gravilla natural de la zona (tonos terraza marina local), 6-30 mm, capa continua e=10 cm, suelta y permeable. Sin malla antimaleza.
BA 12	Masa vegetal (tríadas no lineales de una especie). Etiqueta: código + n° de plantas.
✳	Árbol: copa a tamaño adulto. Etiqueta: código de especie.
☐	Losa de estanques de combustible / elementos existentes: sin plantación, gravilla suelta.
▬	B1 Banca de madera certificada (zona de permanencia tienda).
S/R	Mediana sin ningún riego: jardín mineral de gravilla y rocas del sitio con Copiapoa y lirio del campo (ver nota 7).

NOTAS

1. Diseño conforme al Manual de Diseño de Jardines COPEC V1. Justificación completa en Memoria de Cumplimiento (documento adjunto).
2. Paleta 100 % nativa (23 sp.: 15 endémicas). Material de viveros inscritos en el SAG, preferentemente regionales o de la macrozona (§3.1.2, §3.2.1.4). Formatos Tabla 2. No se autoriza doca (Carpobrotus): monocultivo contrario a §3.3.2, §3.3.1.4 y §3.2.2, riesgo de recibir C. edulis invasora y fruto carnoso que puede atraer roedores (§3.3.2).
3. Sin soleras, pletinas ni separadores interiores (§3.3.1): sólo borde perimetral (solera existente; contra maicillo o tierra, solerilla de hormigón a ras; pletina galvanizada sólo en curvas peatonales; nunca PVC). Gravilla 3-5 cm bajo el canto, directa sobre el suelo: sin malla antimaleza ni geotextil (detalle en L-02).
4. Se eliminan del proyecto original: especies exóticas, bolones y piedra lenteja con mortero, rocas traídas, troncos decorativos, gravilla de color, arena de cuarzo, conchuela y bordillo PVC. Rocas sólo las existentes en el sitio (§3.3.7).
5. Suelo: descompactar; hoyaduras 30x30 / 30x40 / 40x60 cm (Tabla 3); compost maduro NCh2880 hasta 50 % del volumen (suelo arenoso con MO < 1 %); romper costra calcárea si aparece.
6. Franja de visibilidad junto a pistas y accesos: sólo especies de altura adulta <= 0,8 m. P. venusta a >= 1 m y P. chilensis a >= 2 m de bordes de circulación.
7. Riego por goteo autocompensado y antidrenante 2 L/h, un gotero por planta (2 en arbustos de 1,2 m o más de diámetro adulto, 4 en árboles), PE 16 mm, 4 sectores por hidrozona, programador a batería, filtro, regulador y remarcador (cap. 4). Fuente prioritaria: agua reciclada Lavamax, previa validación sanitaria. Mediana S/R: sin ningún riego. Sólo Copiapoa coquimbana y lirio del campo, plantados con las primeras lluvias (cactus mar-may, lirio may-jun); gravilla 10 cm y rocas sueltas del sitio. Hoyaduras con compost reducido (cactáceas 10 % con 50 % de fracción mineral; lirio 20 %). Pérdidas en años secos: reponer en otoño. 2 especies y cobertura ~30 %: desviación de §3.3.2 y §3.2.2 a validar por COPEC.
8. No plantar sobre losa de estanques ni a menos de 0,6 m de cámaras, luminarias, letreros y cargadores EV; árboles a >= 1,5 m. Verificar redes y faja de media tensión (borde oriente) antes de excavar.
9. Patio trasero y estacionamientos de maicillo se mantienen según arquitectura (fuera del alcance de jardín).
10. Ubicaciones y cantidades referenciales: ajustar en terreno según diagnóstico de sitio COPEC (§3.1.1) sin alterar densidades ni composición.

MODIFICACIONES

N°	FECHA	COMENTARIOS	DIB.	REV.
00	20/05/2026	PAISAJISMO ZONA NORTE CENTRAL	BRB	PGM
A	16/10/2026	PAISAJISMO AJUSTADO A MANUAL DE DISEÑO DE JARDINES COPEC V1	IA	GCC
B	19/10/2026	SE ELIMINAN PANELES DE EDUCACIÓN AMBIENTAL E IDENTIFICACIÓN DE ZONA	IA	GCC
C	27/10/2026	RESPUESTA A CONSULTAS DEL CONTRATISTA: MEDIANA SIN RIEGO Y BORDES PERIMETRALES	IA	GCC
D	28/10/2026	MEDIANA S/R SIN NINGÚN RIEGO: JARDÍN MINERAL CON COPIAPOA Y LIRIO DEL CAMPO	IA	GCC

PROPUESTA DE PAISAJISMO SUSTENTABLE

Rediseño de jardines conforme al Manual de Diseño de Jardines COPEC V1 (Paisajismo Ecosistémico COPEC). Base de arquitectura: plano 40000-PN-TONGOY BARRIO INDUSTRIAL-VAG-IC-PY-PJ-PL-001-00 (VIAL AG, 20/05/2026). Se mantiene sin cambios el patio trasero y los estacionamientos de maicillo.

Elaborado por Gestión de Cambio Climático COPEC con asistencia de IA. Requiere validación del paisajista responsable y de COPEC (Manual §1.4) antes de construir.

BASE ARQUITECTURA: VIAL AG (20/05/2026)
PAISAJISMO: PROPUESTA MANUAL JARDINES V1
Gestión de Cambio Climático COPEC

COPEC

PROYECTO: ESTACIÓN DE SERVICIOS Y LOCAL COMERCIAL

DIRECCIÓN:
COMUNA:
ROL Nº:

L-01
PAISAJISMO

40000 TONGOY BARRIO INDUSTRIAL

FECHA **28/10/2026**

CONTENIDO: PLANO DE PAISAJISMO - AJUSTE MANUAL JARDINES COPEC V1

ESCALA **1:250**

CODIGO ARCHIVO NOMENCLATURA COPEC
40000-PN-TONGOY BARRIO INDUSTRIAL-VAG-IC-PY-PJ-PL-001-D.DWG / .DXF / .PDF

REV. D

PLANTA PLAYA

PAISAJISMO SUSTENTABLE - MANUAL DE DISEÑO DE JARDINES COPEC V1

ESC 1:250

1. ZONIFICACIÓN SEGÚN MANUAL §3.3.1

Franjas de visibilidad y zona de permanencia

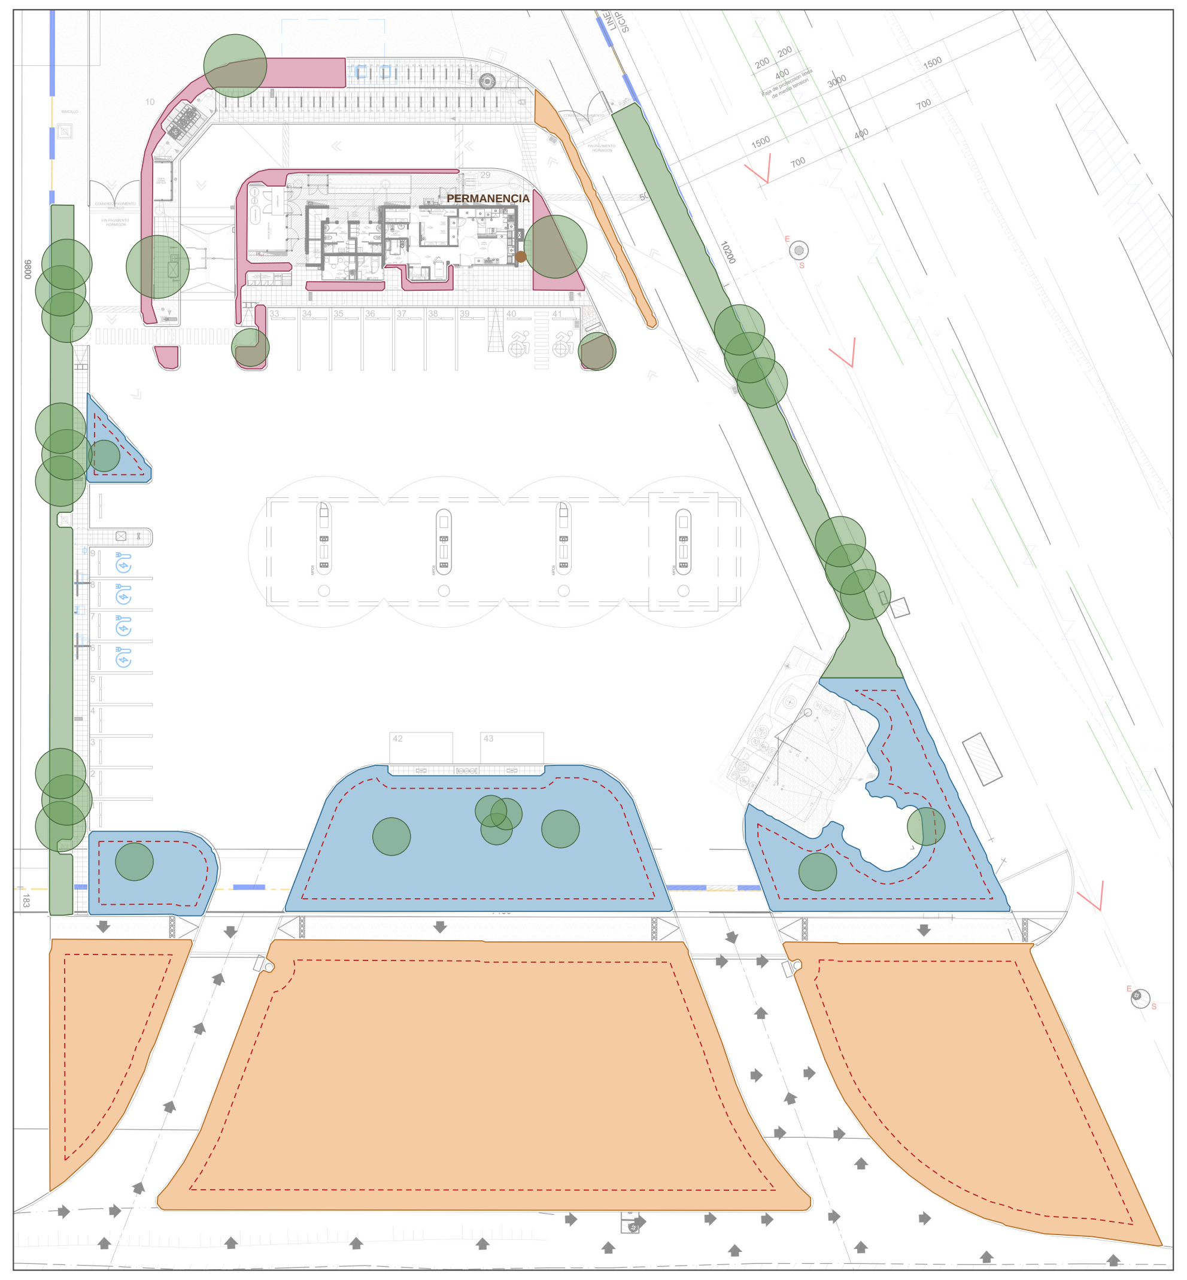

ESC. 1:600

2. COBERTURA INICIAL (AÑO 0)

Plantas al momento de la plantación sobre gravilla natural 10 cm

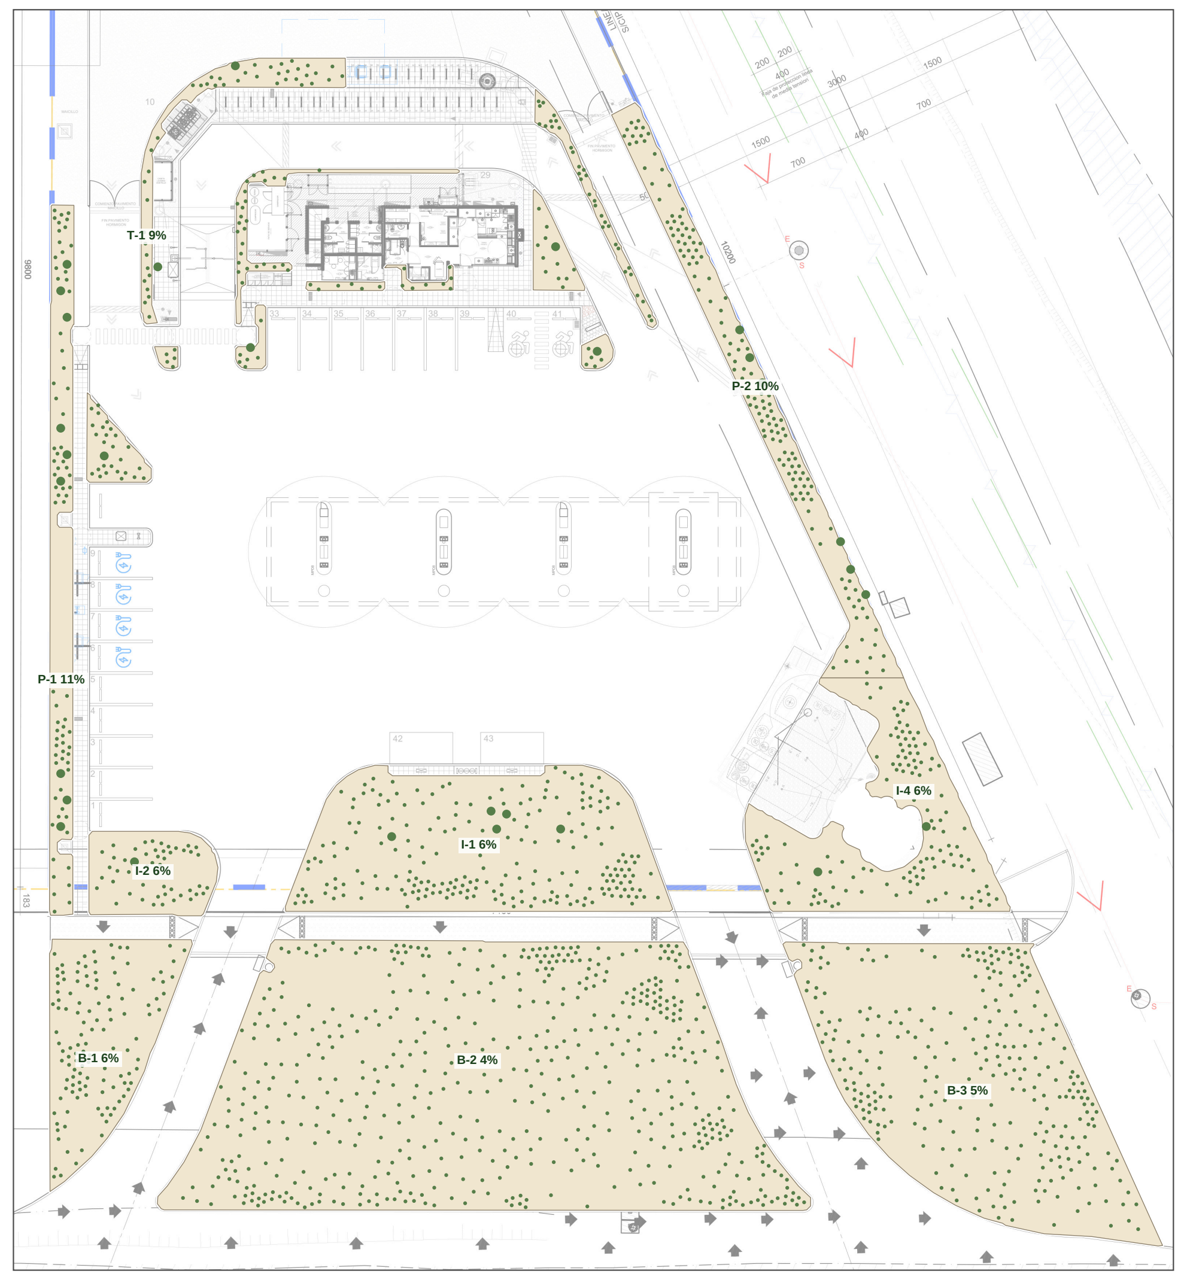

ESC. 1:600

3. COBERTURA DESARROLLADA (AÑO 4-5)

Proyección de copas adultas; % por unidad sobre superficie plantable

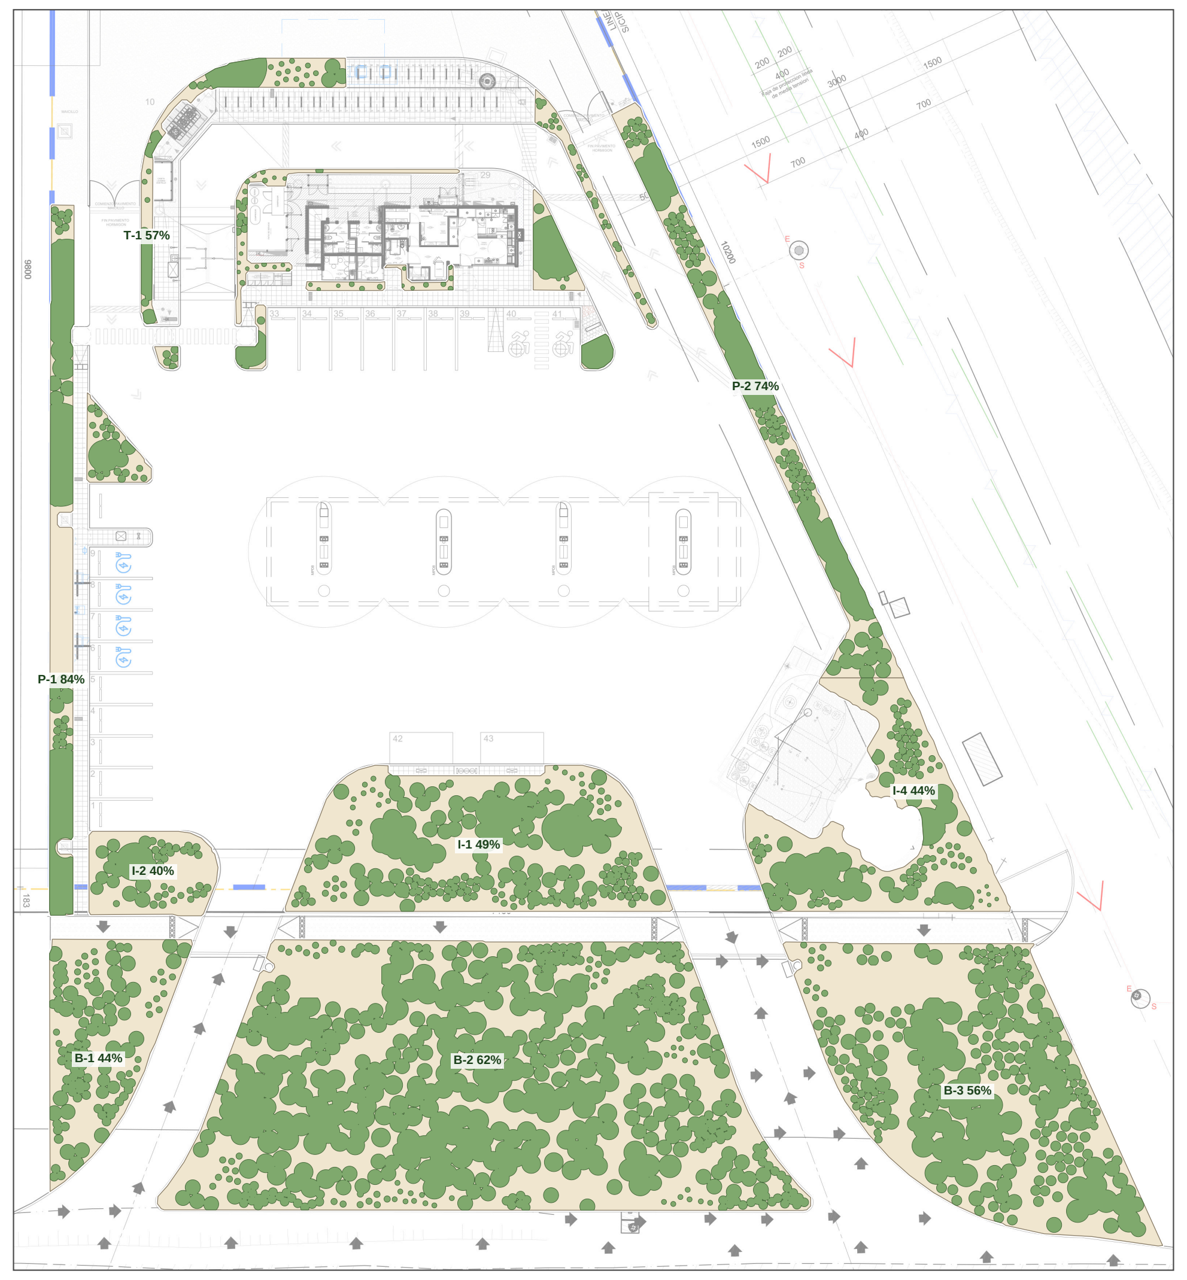

ESC. 1:600

4. RIEGO: HIDROZONAS Y SECTORES

Goteo autocompensado 2 L/h; cabezal junto a caseta Lavamax

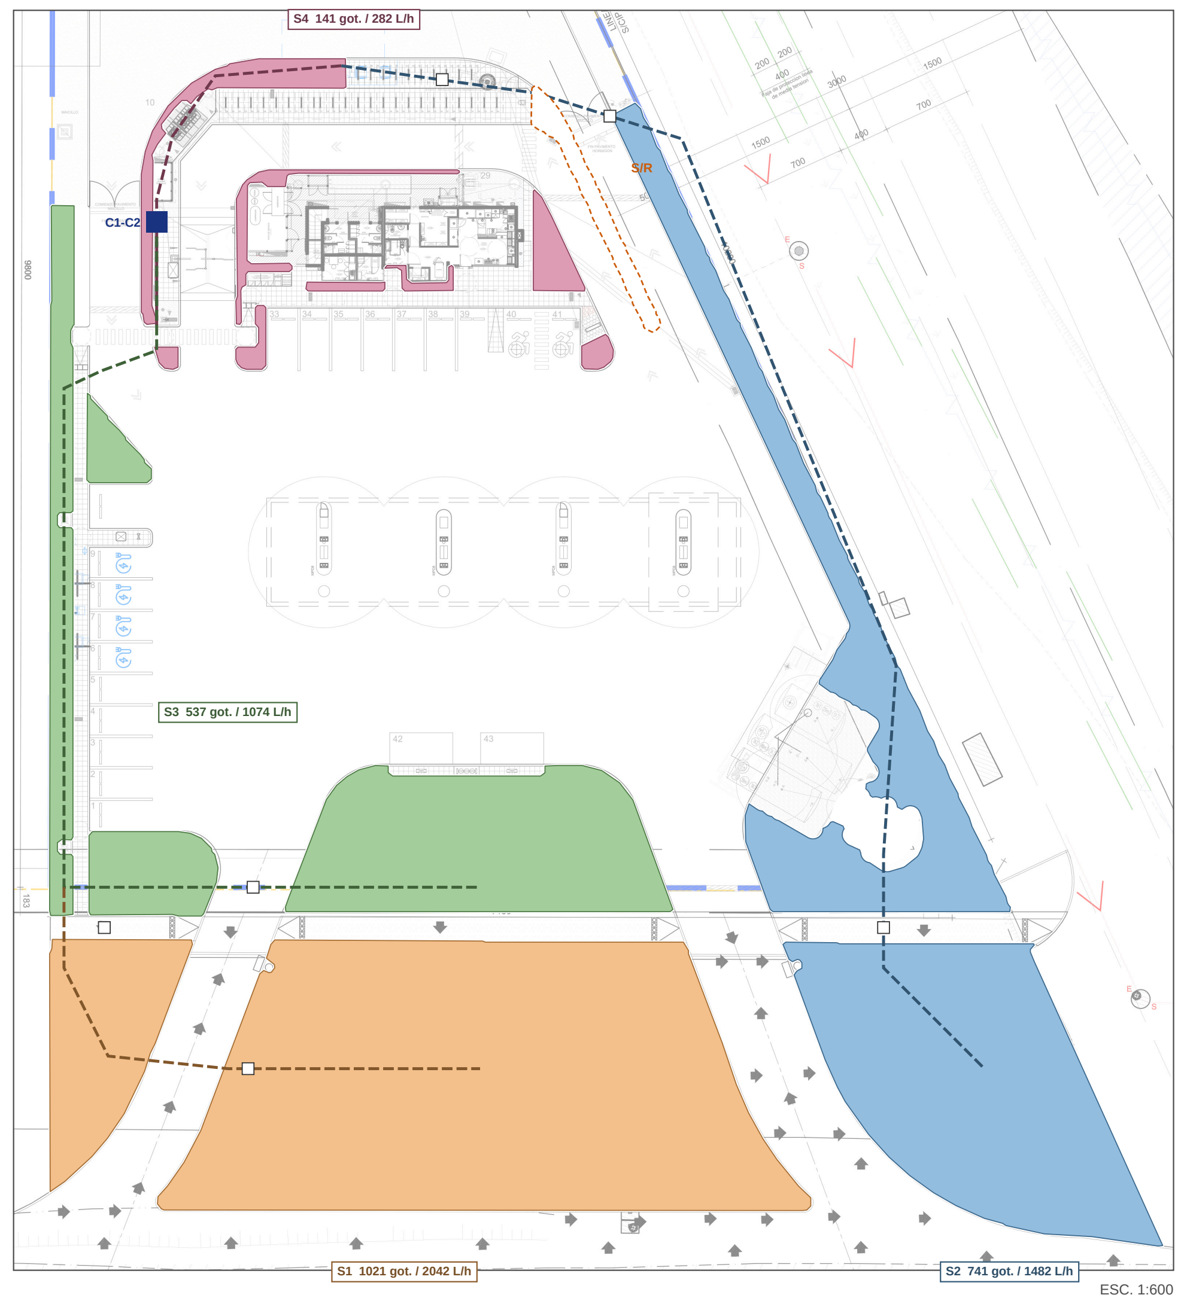

ESC. 1:600

DETALLE 1 - PLANTACIÓN ESTRATO INFERIOR ESC. 1:20

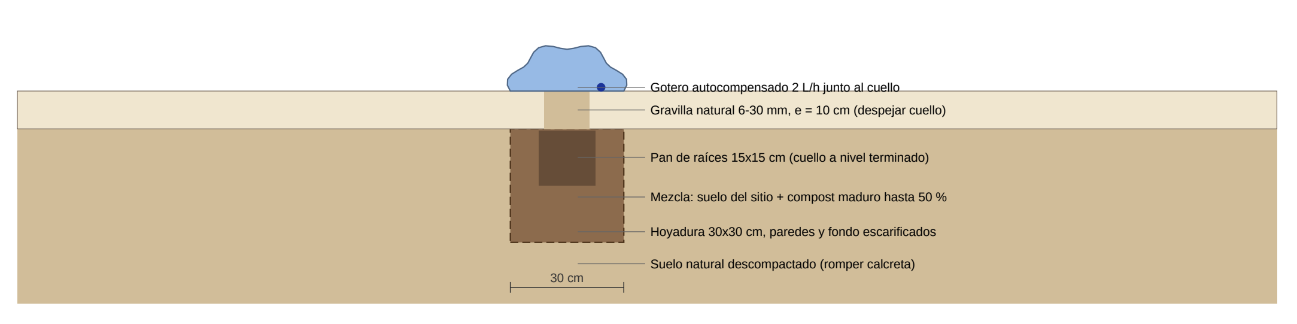
Gotero autocompensado 2 L/h junto al cuello
Gravilla natural 6-30 mm, e = 10 cm (despejar cuello)
Pan de raíces 15x15 cm (cuello a nivel terminado)
Mezcla: suelo del sitio + compost maduro hasta 50 %
Hoyadura 30x30 cm, paredes y fondo escarificados
Suelo natural descompactado (romper calcreta)
30 cm

DETALLE 2 - PLANTACIÓN ESTRATO MEDIO ESC. 1:20

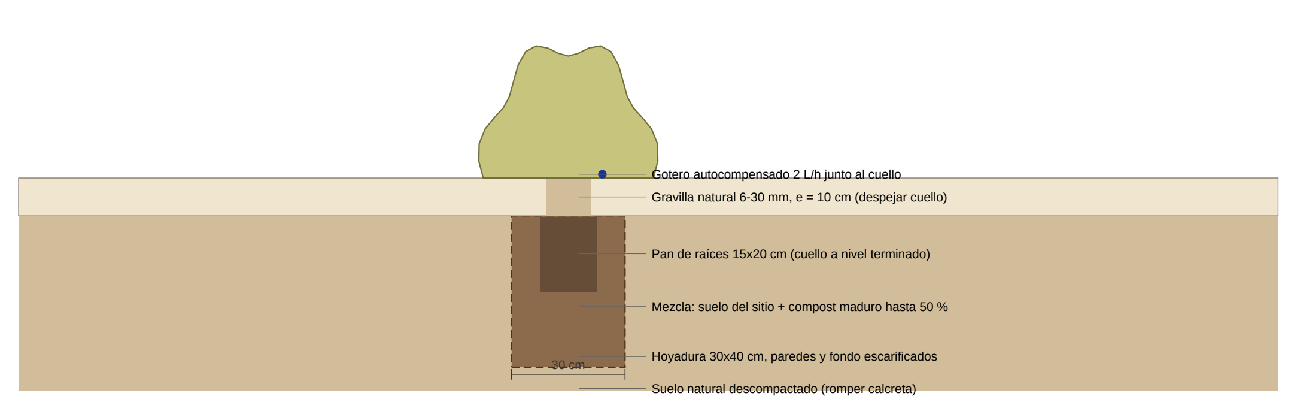
Gotero autocompensado 2 L/h junto al cuello
Gravilla natural 6-30 mm, e = 10 cm (despejar cuello)
Pan de raíces 15x20 cm (cuello a nivel terminado)
Mezcla: suelo del sitio + compost maduro hasta 50 %
Hoyadura 30x40 cm, paredes y fondo escarificados
30 cm
Suelo natural descompactado (romper calcreta)

DETALLE 3 - PLANTACIÓN ESTRATO SUPERIOR ESC. 1:20

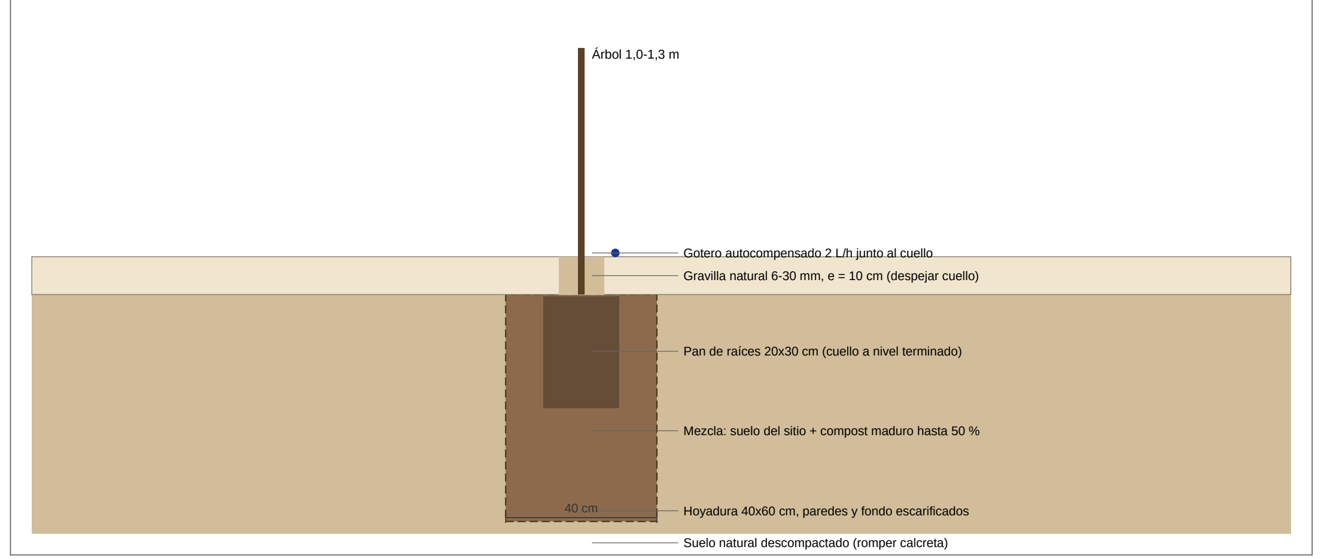
Árbol 1,0-1,3 m
Gotero autocompensado 2 L/h junto al cuello
Gravilla natural 6-30 mm, e = 10 cm (despejar cuello)
Pan de raíces 20x30 cm (cuello a nivel terminado)
Mezcla: suelo del sitio + compost maduro hasta 50 %
40 cm
Hoyadura 40x60 cm, paredes y fondo escarificados
Suelo natural descompactado (romper calcreta)

DETALLE 4 - COBERTURA MINERAL Y BORDE ESC. 1:10

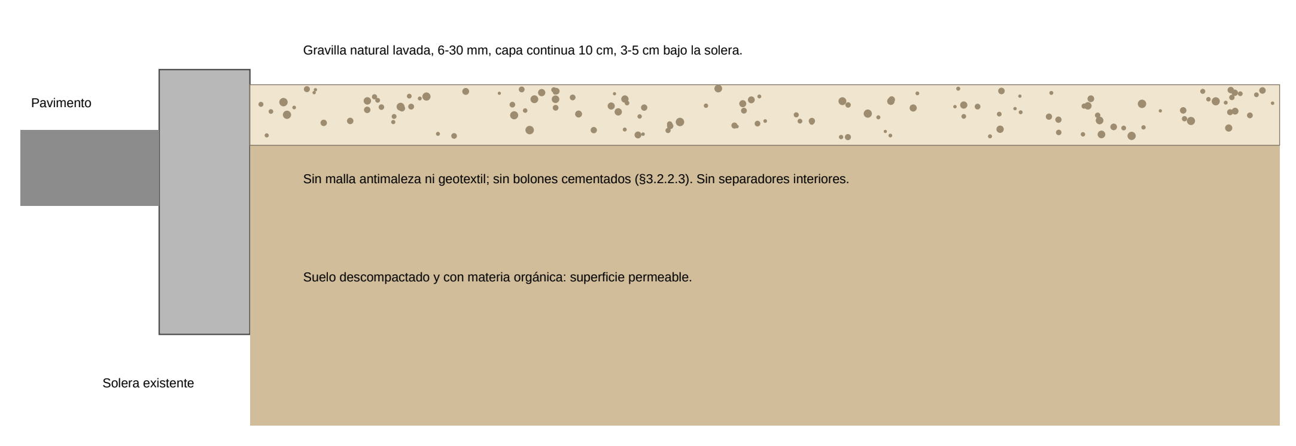
Gravilla natural lavada, 6-30 mm, capa continua 10 cm, 3-5 cm bajo la solera.
Pavimento
Sin malla antimaleza ni geotextil; sin bolones cementados (§3.2.2.3). Sin separadores interiores.
Suelo descompactado y con materia orgánica: superficie permeable.
Solera existente

CORTE A - BANDEJÓN ACCESO/SALIDA ESC. 1:100

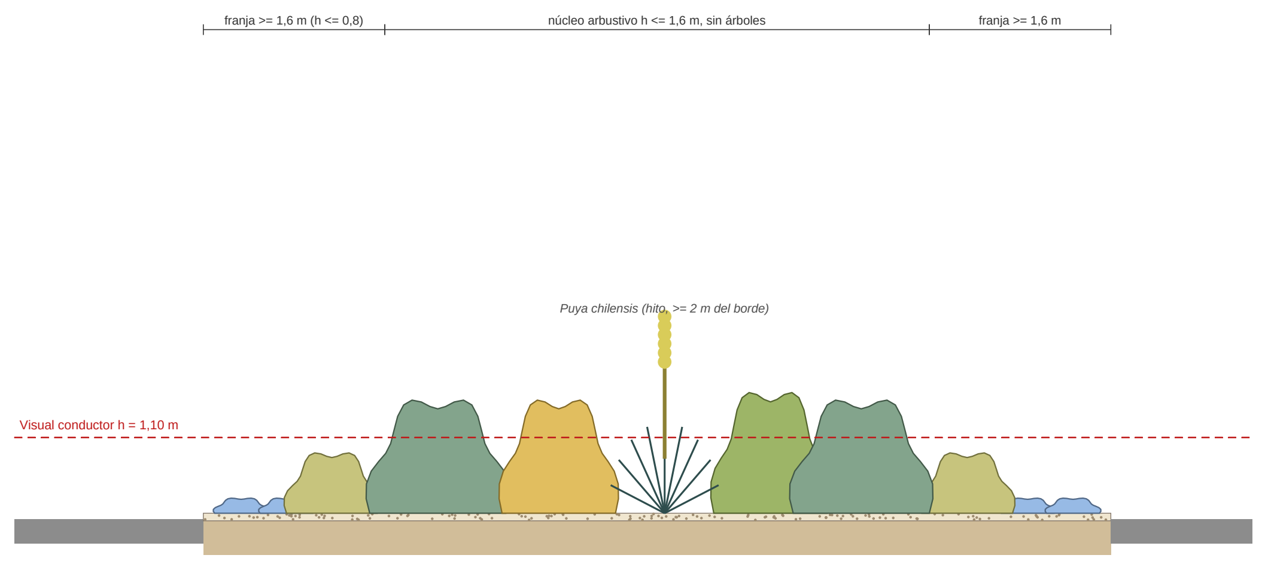
franja >= 1,6 m (h <= 0,8)
núcleo arbustivo h <= 1,6 m, sin árboles
franja >= 1,6 m
Puya chilensis (hito, >= 2 m del borde)
Visual conductor h = 1,10 m

Gravilla natural e=10 cm sobre suelo descompactado; sin malla ni soleras interiores.

CORTE B - ISLA ESC. 1:100

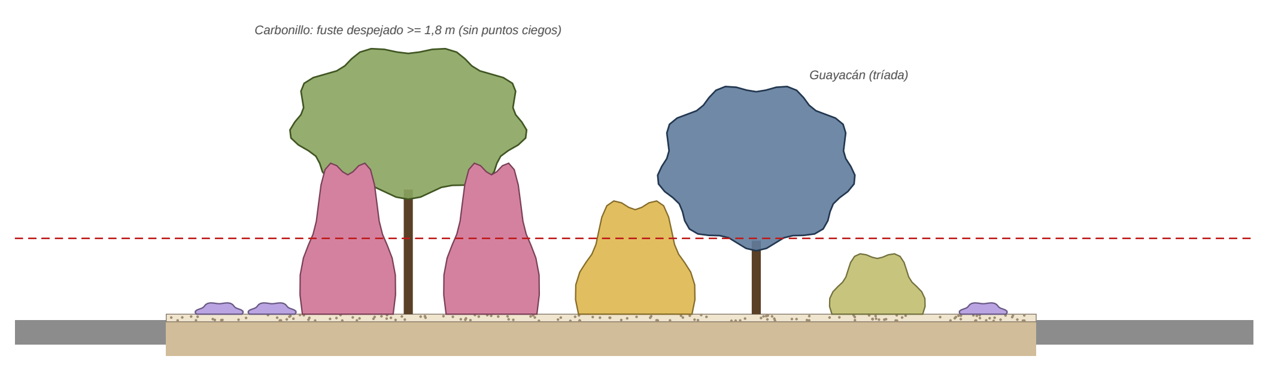

1-2 especies arbóreas de porte controlado; arbustos y cubresuelos en tríadas no lineales.

CORTE C - TIENDA Y PERMANENCIA ESC. 1:100

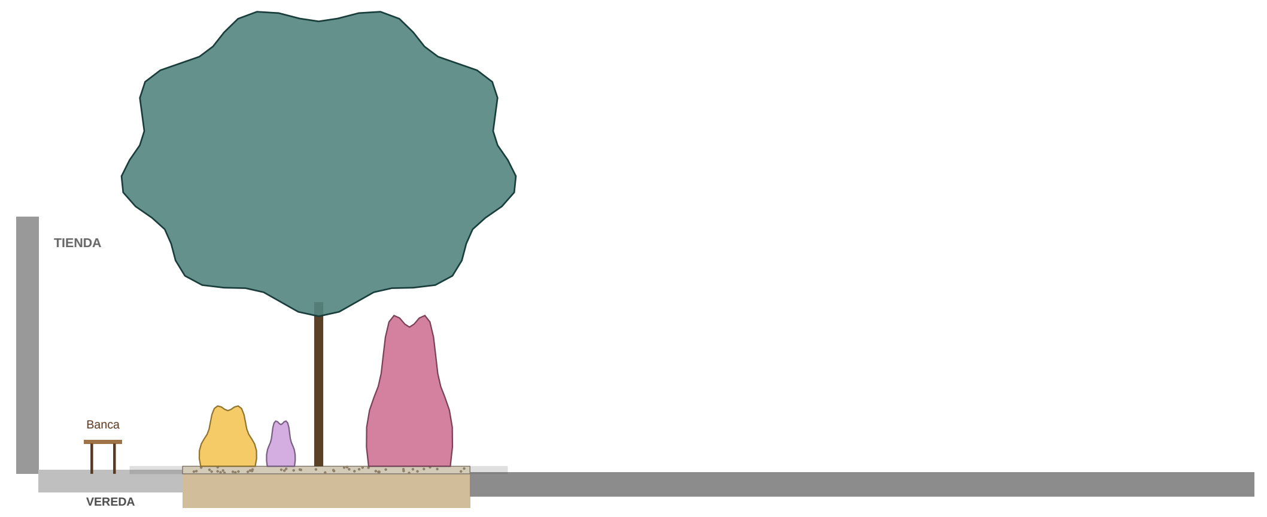

Quillay (sotavento): sombra sobre vereda y banca.

CORTE D - BORDE PERIMETRAL ESC. 1:100

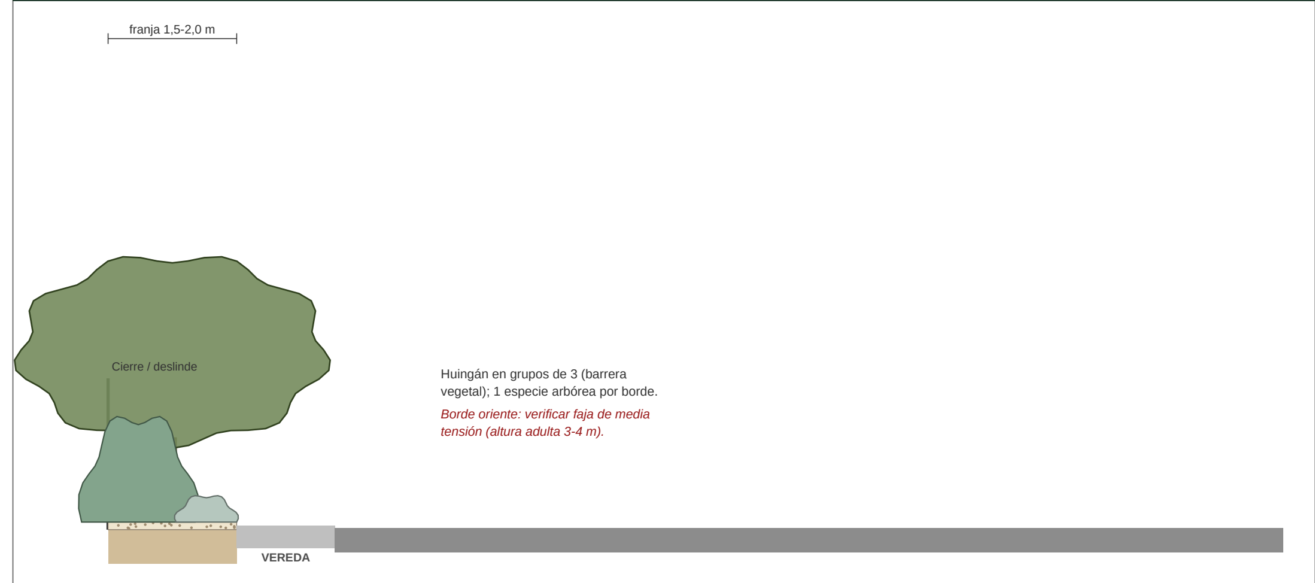
franja 1,5-2,0 m
Cierre / deslinde
Huingán en grupos de 3 (barrera vegetal); 1 especie arbórea por borde.
Borde oriente: verificar faja de media tensión (altura adulta 3-4 m).
VEREDA

ESQUEMA CABEZAL DE RIEGO (Manual §4.3) SIN ESCALA

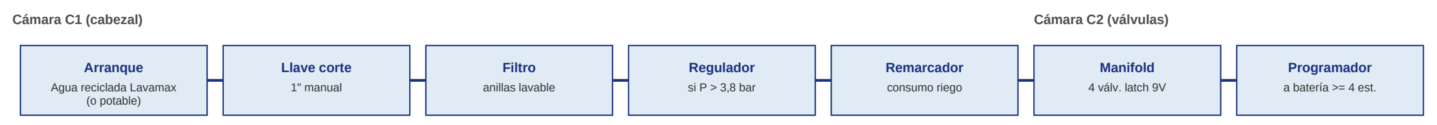

- Acople rápido 32 mm fuera de C1 (emergencias y lavado).
- Matriz PVC hidráulico 32 mm NCh 1635; ramales PE 16 mm UV con gomas bilabiales.
- Goteros autocompensados y antidrenantes 2 L/h; microtubo enterrado bajo gravilla para plantas alejadas.
- Estacas cada 1 m, abrazaderas en uniones, válvula drenante al final de cada ramal.
- Recepción: lavado de redes, prueba de hermeticidad 45 min con zanjas abiertas y carpeta as-built DWG/PDF.

CUADRO DE CUBICACIÓN REFERENCIAL

Plantas bolsa 15x15 cm (herbáceas y cubresuelos)	**930 u**
Plantas bolsa 15x20 cm (arbustos y suculentas)	**773 u**
Cactáceas maceta 10-14 cm (origen de vivero)	**14 u**
Árboles bolsa 20x30 cm, 1,0-1,3 m	**29 u**
Superficie de jardín plantable	**2247 m²**
Gravilla natural 6-30 mm, e = 10 cm (+5 %)	**236 m³**
Excavación de hoyaduras (Tabla 3)	**56.1 m³**
Compost maduro NCh2880 (50 % hoyadura; mediana S/R 10-20 %)	**27.7 m³**
Goteros autocompensados 2 L/h	**2440 u**
Plansa PE 16 mm UV (estimado)	**2163 m**
Matriz PVC 32 mm (esquemática +10 %)	**310 m**
Válvulas solenoides con solenoide latch 9V	**4 u**
Programador a batería >= 4 estaciones	**1 u**
Filtro anillas / regulador / remarcador / acople 32 mm	**1 / 1 / 1 / 1 u**
Cámaras de riego registrables (C1, C2)	**2 u**
Banca de madera certificada	**1 u**
Rocas sueltas del sitio en mediana S/R (15-40 cm)	**según excavación**

Cantidades referenciales para presupuesto; verificar en terreno.

SECTORES DE RIEGO E HIDROZONAS

SECTOR	UNIDADES	HIDROZONA	PLANTAS	GOTEROS	CAUDAL L/h	SUP. VEG. m²	T. PULSO*
● S1	B-1, B-2	Baja	670	1021	2042	660	3h 14min
● S2	B-3, I-4, P-2	Baja	547	741	1482	423	2h 51min
● S3	I-1, I-2, I-3, P-1	Baja (con árboles)	380	537	1074	255	2h 22min
● S4	T-1, T-2, T-3, T-4, T-5, T-6, T-7	Baja-media	116	141	282	55	1h 57min

** Tiempo para aplicar el pulso de 10 L/m² (Tabla 8, Coquimbo) sobre la superficie vegetada con 1 gotero de 2 L/h por planta (2 en arbustos >= 1,2 m de diámetro adulto, 4 en árboles). Dividir en 2 ciclos si hay escurrimiento.*

RÉGIMEN DE RIEGO REGIÓN DE COQUIMBO (Manual Tabla 8) - pulso 10 L/m², frecuencia en días

AÑO	DIC	ENE	FEB	MAR	ABR	MAY	JUN	JUL	AGO	SEP	OCT	NOV
1er año	Cada 5	Cada 10	Cada 15	Cada 15	Cada 15	Cada 10	Cada 5					
2do año	Cada 7	Cada 10	Cada 15	Cada 30	Cada 15	Cada 10						
3er año	Cada 10	Cada 15	Cada 20	Cada 30	Cada 15							
4to a 6to año	Cada 15	Cada 30	Cada 45	Cada 20	Cada 15							
Luego 6to año	Cada 30	Cada 30										

Meses sin valor: sin riego programado (lluvias invernales y camanchaca); ajustar según respuesta de las plantas, restricciones hídricas y lectura del remarcador.

MATRIZ DE MANTENCIÓN (Manual Tabla 20)

COMPONENTE / TAREA	FRECUENCIA	RESP.
Limpieza de filtro central de cabecera	Quincenal / semanal con agua reciclada	EDS
Inspección visual de emisores y líneas	Mensual	EDS
Control fitosanitario y desmalezado manual	Mensual	EDS
Reposición y nivelación de gravilla (10 cm)	Semestral	EDS
Reemplazo de baterías de programador	Anual	EDS
Poda de seguridad y despeje operacional	Según necesidad	EDS
Aplicación de compost / enmienda orgánica	Anual (otoño/primavera)	EDS

- Prohibidos pesticidas de franja roja/amarilla; control mecánico y biocontroladores (§5.1.6).
- Poda sólo sanitaria y de seguridad vial; prohibidas podas geométricas y en floración (§5.1.4).
- Desmalezar sólo especies invasoras (Malva, Chenopodium, kikuyo, correhuela, ailanto).
- Reposiciones con la misma especie nativa; registrar mortalidad por especie (§6.1.5).
- Seguimiento con matriz de evaluación §6.2 (agua, riego, vegetación, flora, suelo, biodiversidad).

ZONIFICACIÓN, COBERTURAS, RIEGO Y DETALLES

PAISAJISMO SUSTENTABLE - MANUAL DE DISEÑO DE JARDINES COPEC V1 - EDS 40000 TONGOY BARRIO INDUSTRIAL

LÁMINA L-02 - CRITERIOS DEL MANUAL

TIPOLOGÍAS DE ZONA (§3.3.1)

🟧 **BANDEJÓN ACCESO/SALIDA**
Sin árboles; estrato medio y bajo; franjas de visibilidad <= 0,8 m.

🟦 **ISLAS**
1-2 especies arbóreas de porte controlado; sin puntos ciegos.

🟥 **TIENDA Y TERRAZA**
2-5 especies arbóreas; sombra y permanencia.

🟩 **BORDES PERIMETRALES**
1 especie arbórea como barrera vegetal.

— Límite franja de visibilidad (hacia pistas sólo h <= 0,8 m)

○ Copa adulta de árboles

COBERTURA INICIAL VS. DESARROLLADA (§3.2.2)

▨ Gravilla natural (espacio abierto, permeable)

● Planta al momento de plantar (bolsa 15-20 cm)

🟩 Cobertura vegetal desarrollada (año 4-5)

Resultado ponderado: cobertura inicial 6 % -> desarrollada 57 % (meta Manual ~60 %, hasta 80 %). Las superficies minerales visibles disminuyen a medida que crecen las masas; la gravilla protege el suelo mientras tanto.

SECTORES DE RIEGO (cap. 4)

🟧 **S1 - Bandejones poniente y central**
Hidrozona baja · B-1, B-2

🟦 **S2 - Oriente: bandejón, isla estanques y borde**
Hidrozona baja · B-3, I-4, P-2

🟩 **S3 - Islas y borde poniente**
Hidrozona baja (con árboles) · I-1, I-2, I-3, P-1

🟥 **S4 - Tienda y terraza**
Hidrozona baja-media · T-1, T-2, T-3, T-4, T-5, T-6, T-7

☐ **S/R - Mediana acceso patio SIN NINGÚN RIEGO**
Jardín mineral: Copiapoa y lirio del campo, sólo lluvia; plantar con las primeras lluvias

– – – Matriz PVC 32 mm (trazado esquemático)

☐ Camisa bajo pista/pavimento (coordinar con Ingeniería §4.2)

■ C1-C2 cámaras de cabezal y válvulas junto a caseta Lavamax

VERIFICACIÓN RÁPIDA DEL ESTÁNDAR

Especies nativas / exóticas	**23 / 0**
Especies por unidad paisajística (4-8; unidades > 20 m²)	**4-8**
Densidad media (ref. 0,6 pl/m²)	**0.78 pl/m²**
Cobertura desarrollada (~60 %)	**57 %**
Árboles en bandejones	**0**
Sp. arbóreas en islas (1-2)	**2 (carbonillo, guayacán)**
Sp. arbóreas en tienda (2-5)	**3 (molle, quillay, carbonillo)**
Sp. arbórea en bordes (1)	**1 (huingán)**
Césped / malla / soleras interiores	**No / No / No**
Gravilla natural e = 10 cm, sin malla	**Sí**
Goteo autocompensado 2 L/h	**Sí (salvo mediana S/R)**
Doca (Carpobrotus)	**No**
Frutos carnosos grandes o a ras de suelo	**No**

MODIFICACIONES

N°	FECHA	COMENTARIOS	DIB.	REV.
00	20/05/2026	PAISAJISMO ZONA NORTE CENTRAL	BRB	PGM
A	16/10/2026	PAISAJISMO AJUSTADO A MANUAL DE DISEÑO DE JARDINES COPEC V1	IA	GCC
B	19/10/2026	SE ELIMINAN PANELES DE EDUCACIÓN AMBIENTAL E IDENTIFICACIÓN DE ZONA	IA	GCC
C	27/10/2026	RESPUESTA A CONSULTAS DEL CONTRATISTA: MEDIANA SIN RIEGO Y BORDES PERIMETRALES	IA	GCC
D	28/10/2026	MEDIANA S/R SIN NINGÚN RIEGO: JARDÍN MINERAL CON COPIAPOA Y LIRIO DEL CAMPO	IA	GCC

PROPUESTA DE PAISAJISMO SUSTENTABLE

Rediseño de jardines conforme al Manual de Diseño de Jardines COPEC V1 (Paisajismo Ecosistémico COPEC). Base de arquitectura: plano 40000-PN-TONGOY BARRIO INDUSTRIAL-VAG-IC-PY-PJ-PL-001-00 (VIAL AG, 20/05/2026). Se mantiene sin cambios el patio trasero y los estacionamientos de maicillo.

Elaborado por Gestión de Cambio Climático COPEC con asistencia de IA. Requiere validación del paisajista responsable y de COPEC (Manual §1.4) antes de construir.

BASE ARQUITECTURA: VIAL AG (20/05/2026)
PAISAJISMO: PROPUESTA MANUAL JARDINES V1
Gestión de Cambio Climático COPEC

COPEC

PROYECTO: ESTACIÓN DE SERVICIOS Y LOCAL COMERCIAL

DIRECCIÓN:
COMUNA:
ROL Nº:

L-02
PAISAJISMO

40000 TONGOY BARRIO INDUSTRIAL

FECHA **28/10/2026**

CONTENIDO: ZONIFICACIÓN, COBERTURAS, RIEGO Y DETALLES

ESCALA **INDICADA**

CODIGO ARCHIVO NOMENCLATURA COPEC
40000-PN-TONGOY BARRIO INDUSTRIAL-VAG-IC-PY-PJ-PL-002-D.DWG / .DXF / .PDF

REV. D